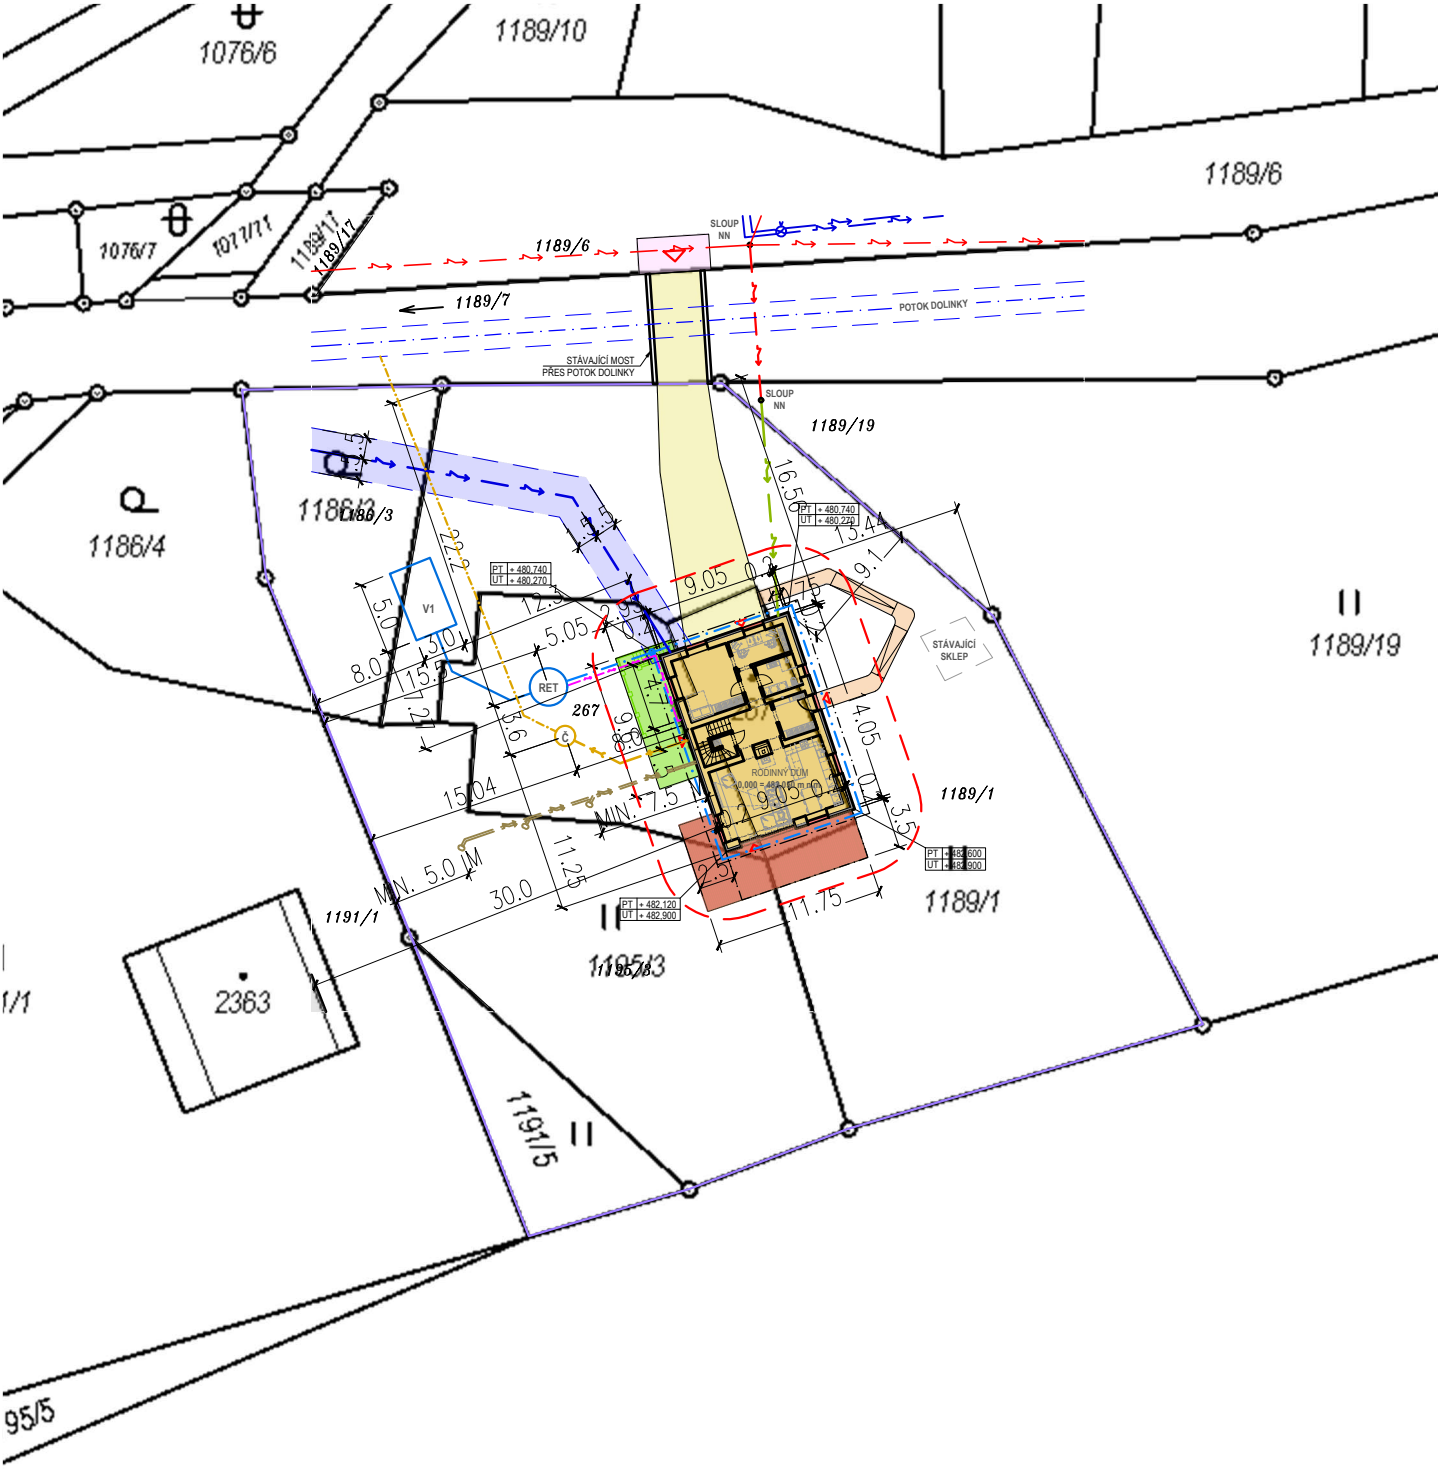

0,000 = 483,050 m n.m.

TATO DOKUMENTACE SLOUŽÍ VÝHRADNĚ K ZÍSKÁNÍ STAVEBNÍHO POVOLENÍ DANÉ STAVBY A JAKÉKOLIV POUŽITÍ NAD RÁMEC TOHOTO ROZSAHU JE NA VLASTNÍ ZODPOVĚDNOST INVESTORA NEBO ZHOTOVITELE STAVBY. PRO ZHOTOVENÍ JE NUTNO ZPRACOVAT REALIZAČNÍ DOKUMENTACI.

HRANICE ŘEŠENÝCH PARCEL VE VLASTNICTVÍ INVESTORA

POZNÁMKA:

JEDNÁ SE O CELKOVOU REKONSTRUKCI PŮVODNÍHO OBJEKTU, VEŠKERÉ SKLADBY KONSTRUCKÍ JE TŘEBA PO ODKRYTÍ ZKONTROLOVAT A PŘÍPADNÉ ODCHYLKY ŘEŠIT S PROJEKTANTEM NEBO STATIKEM. VEŠKERÉ DETAILY NEBO ODCHYLKY OD PROJEKTU NUTNO ŘEŠIT S PROJEKTANTEM STAVBY PŘED SAMOTNOU REALIZACÍ. DOPORUČUJEME ZPRACOVAT REALIZAČNÍ PROJEKT S PROVEDENÍM SOND DO KONSTRUKCÍ STAVBY. VEŠKERÉ VÝŠKOVÉ ROZMĚRY V NOVÉM STAVU JSOU VZTAŽENY K NOVÉ VÝŠCE PODLAHY 0,000. VEŠKERÉ ROZMĚRY JE NUTNO ZAMĚŘIT PŘESNĚ NA STAVBĚ !!! PŘEKLADY V NENOSNÝCH STĚNÁCH ŘEŠIT SYSTÉMOVĚ V TL. STĚNY !!! VŠECHNY VÝPLNĚ OTVORŮ V OBVODOVÉ STĚNĚ OSADIT NA VNĚJŠÍ LÍC ZDIVA A PŘETÁHNOUT ZATEPLENÍ FASÁDY O 20 MM PŘES OKENNÍ RÁM. NUTNO OSADIT KASTLÝKY ŽALUZIÍ SE STEJNÝM PŘESAHEM.

[redacted]

ČÁST:	C - SITUAČNÍ VÝKRESY	MĚŘÍTKO	1 : 500
VÝKRES:	KATASTRÁLNÍ SITUAČNÍ VÝKRES	ČÍSLO	C.2