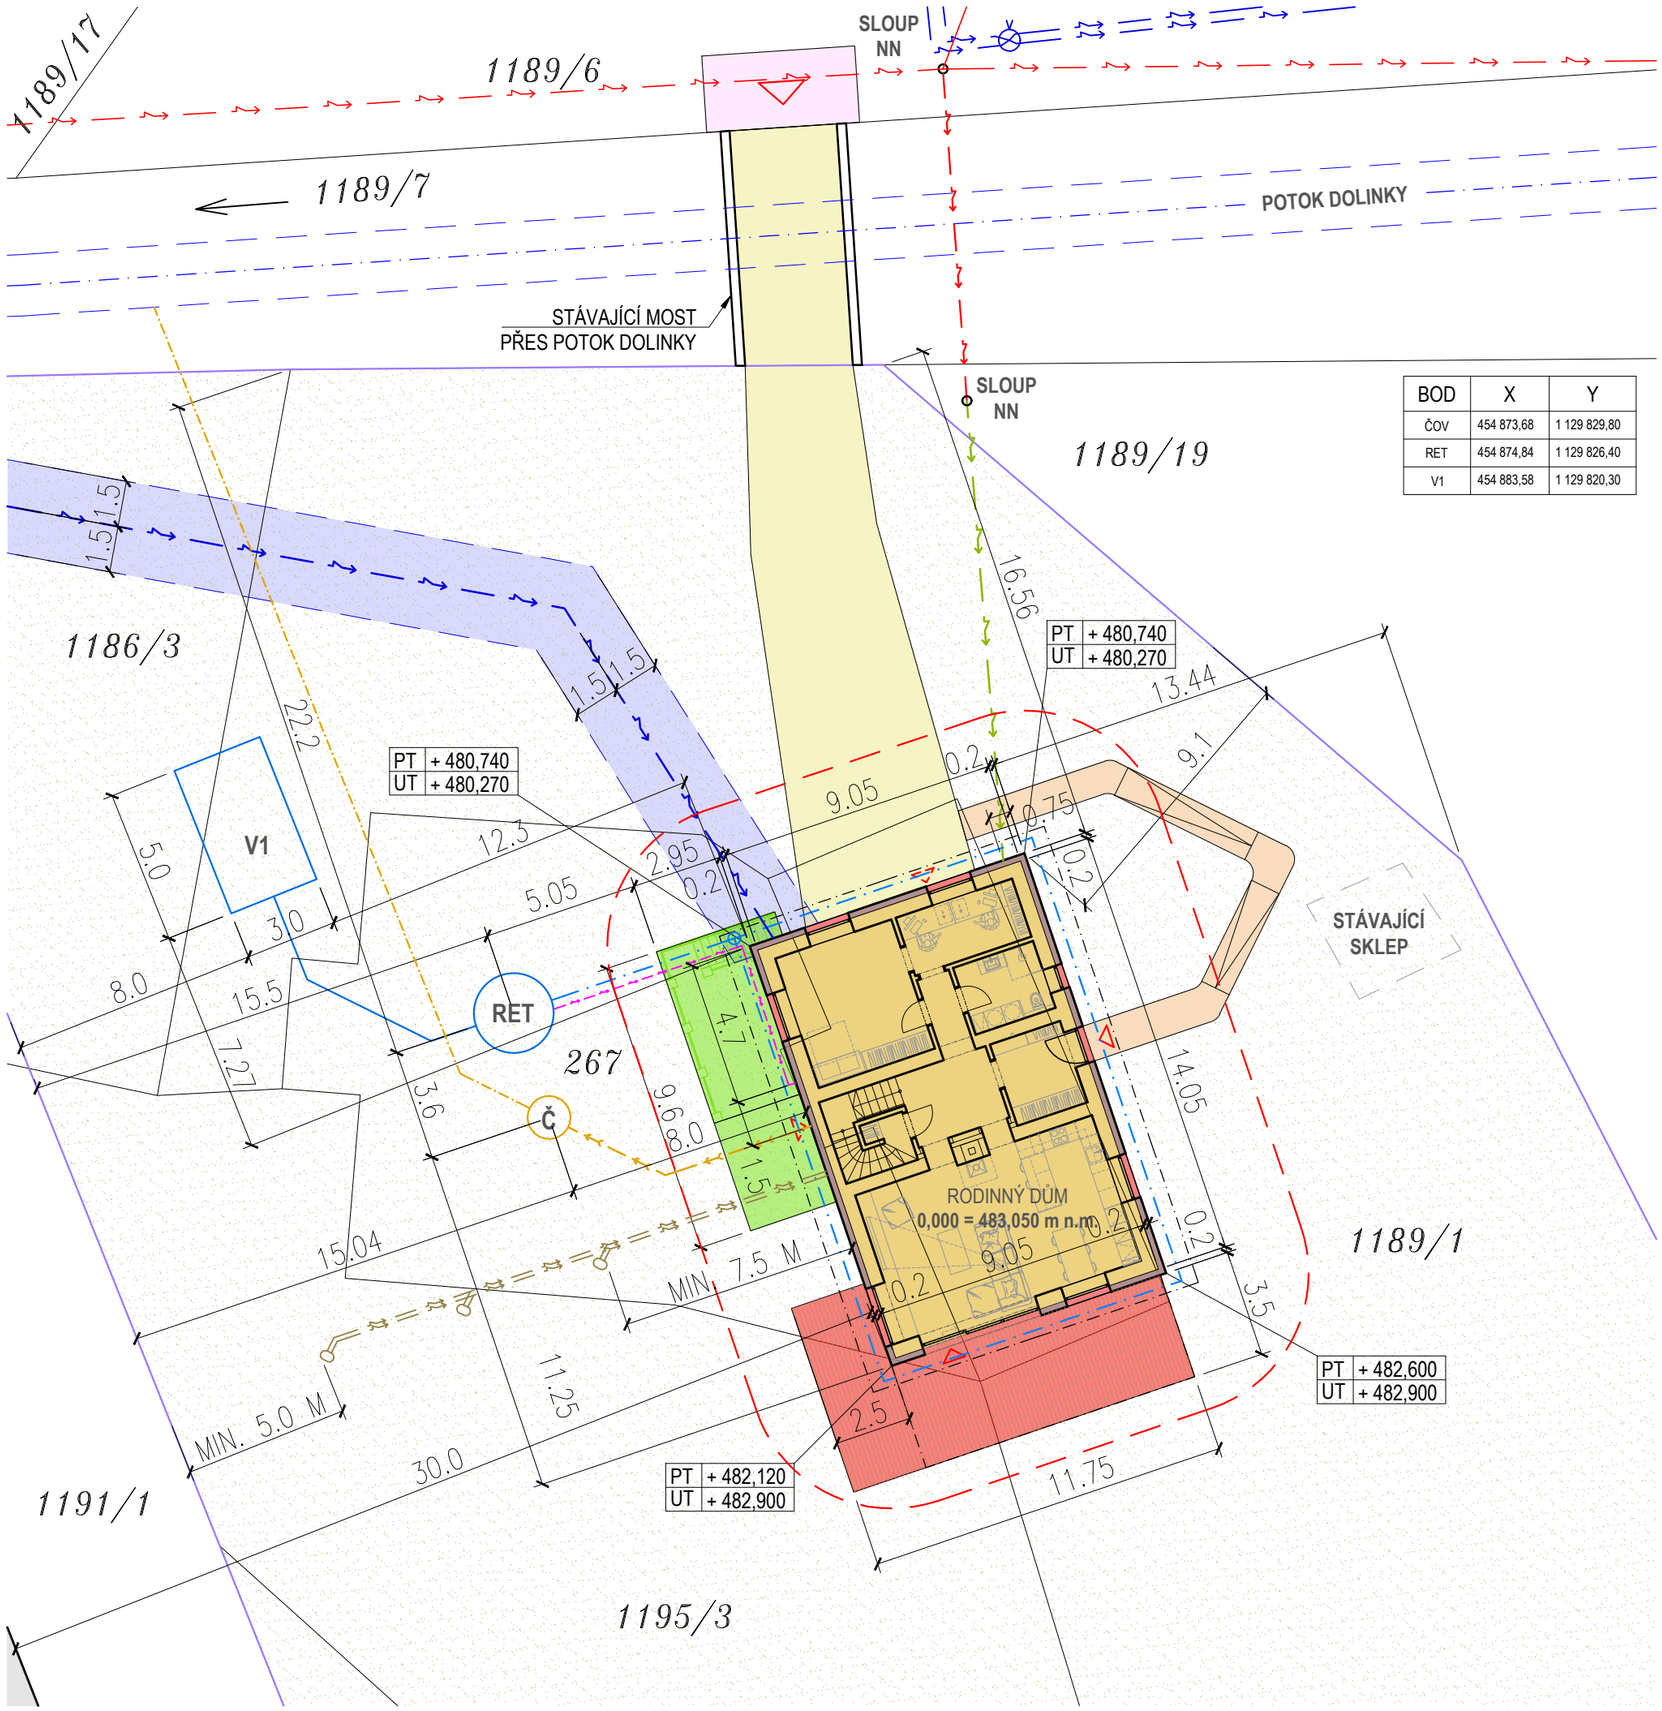

BOD	X	Y
ČOV	454 873,68	1 129 829,80
RET	454 874,84	1 129 826,40
V1	454 883,58	1 129 820,30

LEGENDA NAVRHOVANÝCH PLOCH

- OKOLNÍ STAVBY RD
- PŮVODNÍ ŘEŠENÉ RD - STAVEBNÍ ÚPRAVY
- PŮVODNÍ ŘEŠENÉ RD - DEMOLICE
- ŘEŠENÉ RD - NOVÉ ZATEPLENÍ A TERASA
- NOVÉ ZPEVNĚNÉ PLOCHY - CHODNÍK KE VSTUPU
- PŮVODNÍ SKLEP - NENÍ PŘEDMĚTEM PD
- STÁVAJÍCÍ ZPEVNĚNÉ PLOCHY - NENÍ PŘEDMĚTEM PD
- STÁVAJÍCÍ DOPRAVNÍ NAPOJENÍ - NENÍ PŘEDMĚTEM PD
- PNP - 4,65 M - VIZ. PBŘ - NEPŘESAHUJE POZEMKY INVESTORA

LEGENDA KATASTRÁLNÍCH ČAR A ZNAČEK

- HRANICE POZEMKŮ INVESTORA PARC. Č. 1186/3, 267, 1195/3, 1191/5, 1189/1
- POTOK DOLINKY

LEGENDA INŽENÝRSKÝCH SÍTÍ

- NN - NADZEMNÍ VEDENÍ ELEKTRICKÝCH KABELŮ - ČEZ DISTRIBUCE
- VEDENÍ VODOVODNÍHO ŘADU A PŘÍPOJKY K OKOLNÍM RD - OVaK

LEGENDA STÁVAJÍCÍCH PŘIPOJOVACÍCH POTRUBÍ A MÉDIÍ OBJEKTU RD

- STÁVAJÍCÍ NADZEMNÍ PŘÍPOJKA NN - ČEZ
- STÁVAJÍCÍ PODZEMNÍ PŘÍPOJKA VODY - DN 25 - 1"PE

LEGENDA NOVÝCH PŘIPOJOVACÍCH POTRUBÍ A MÉDIÍ OBJEKTU RD

- NOVÁ PODZEMNÍ PŘÍPOJKA NN - CYKY 5x1,5; CYKY 3x1,5; UTP; CYKY 4x10 - 15,0 M
- DEŠŤOVÁ VODA Z RETENCE PRO POTŘEBY WC - DN 25 - 1"PE - 11,5 M
- NOVÁ DEŠŤOVÁ KANALIZACE A DREÁŽ OKOLO STAVBY - HT 160 - 57,3 M
- NOVÝ ROZVOD VNĚJŠÍ KANALIZACE NAPOJENÝ DO ČOV - HT 160 - 8,5 M
- NOVÝ ROZVOD PŘEČIŠTĚNÉ VODY Z ČOV DO VODOTEČE - HT 160 - 30,0 M
- NOVÝ ROZVOD DEŠŤOVÉ VODY Z RETENCE DO VSAKU V1 - HT 160 - 9,0 M
- NOVÝ ROZVOD Z TČ DO PODZEMNÍCH VRTŮ BUDE UPŘESNĚNO DODAVATELEM

POZNÁMKA:

JEDNÁ SE O CELKOVOU REKONSTRUKCI PŮVODNÍHO OBJEKTU, VEŠKERÉ SKLADBY KONSTRUCKÍ JE TŘEBA PO ODKRYTÍ ZKONTROLOVAT A PŘÍPADNÉ ODCHYLKY ŘEŠIT S PROJEKTANTEM NEBO STATIKEM. VEŠKERÉ DETAILY NEBO ODCHYLKY OD PROJEKTU NUTNO ŘEŠIT S PROJEKTANTEM STAVBY PŘED SAMOTNOU REALIZACÍ. DOPORUČUJEME ZPRACOVAT REALIZAČNÍ PROJEKT S PROVEDENÍM SOND DO KONSTRUKCÍ STAVBY. VEŠKERÉ VÝŠKOVÉ ROZMĚRY V NOVÉM STAVU JSOU VZTAŽENY K NOVÉ VÝŠCE PODLAHY 0,000. VEŠKERÉ ROZMĚRY JE NUTNO ZAMĚŘIT PŘESNĚ NA STAVBĚ !!! PŘEKLADY V NENOSNÝCH STĚNÁCH ŘEŠIT SYSTÉMOVĚ V TL. STĚNY !!! VŠECHNY VÝPLNĚ OTVORŮ V OBVODOVÉ STĚNĚ OSADIT NA VNĚJŠÍ LÍC ZDIVA A PŘETÁHNOUT ZATEPLENÍ FASÁDY O 20 MM PŘES OKENNÍ RÁM. NUTNO OSADIT KASTLÝKY ŽALUZIÍ SE STEJNÝM PŘESAHEM.

0,000 = 483,050 m n.m.

TATO DOKUMENTACE SLOUŽÍ VÝHRADNĚ K ZÍSKÁNÍ STAVEBNÍHO POVOLENÍ DANÉ STAVBY A JAKÉKOLIV POUŽITÍ NAD RÁMEC TOHOTO ROZSAHU JE NA VLASTNÍ ZODPOVĚDNOST INVESTORA NEBO ZHOTOVITELE STAVBY. PRO ZHOTOVENÍ JE NUTNO ZPRACOVAT REALIZAČNÍ DOKUMENTACI.

[redacted]

ČÁST:	C - SITUAČNÍ VÝKRESY	MĚŘÍTKO	1 : 250
VÝKRES:	KOORDINAČNÍ SITUAČNÍ VÝKRES	ČÍSLO	C.3